


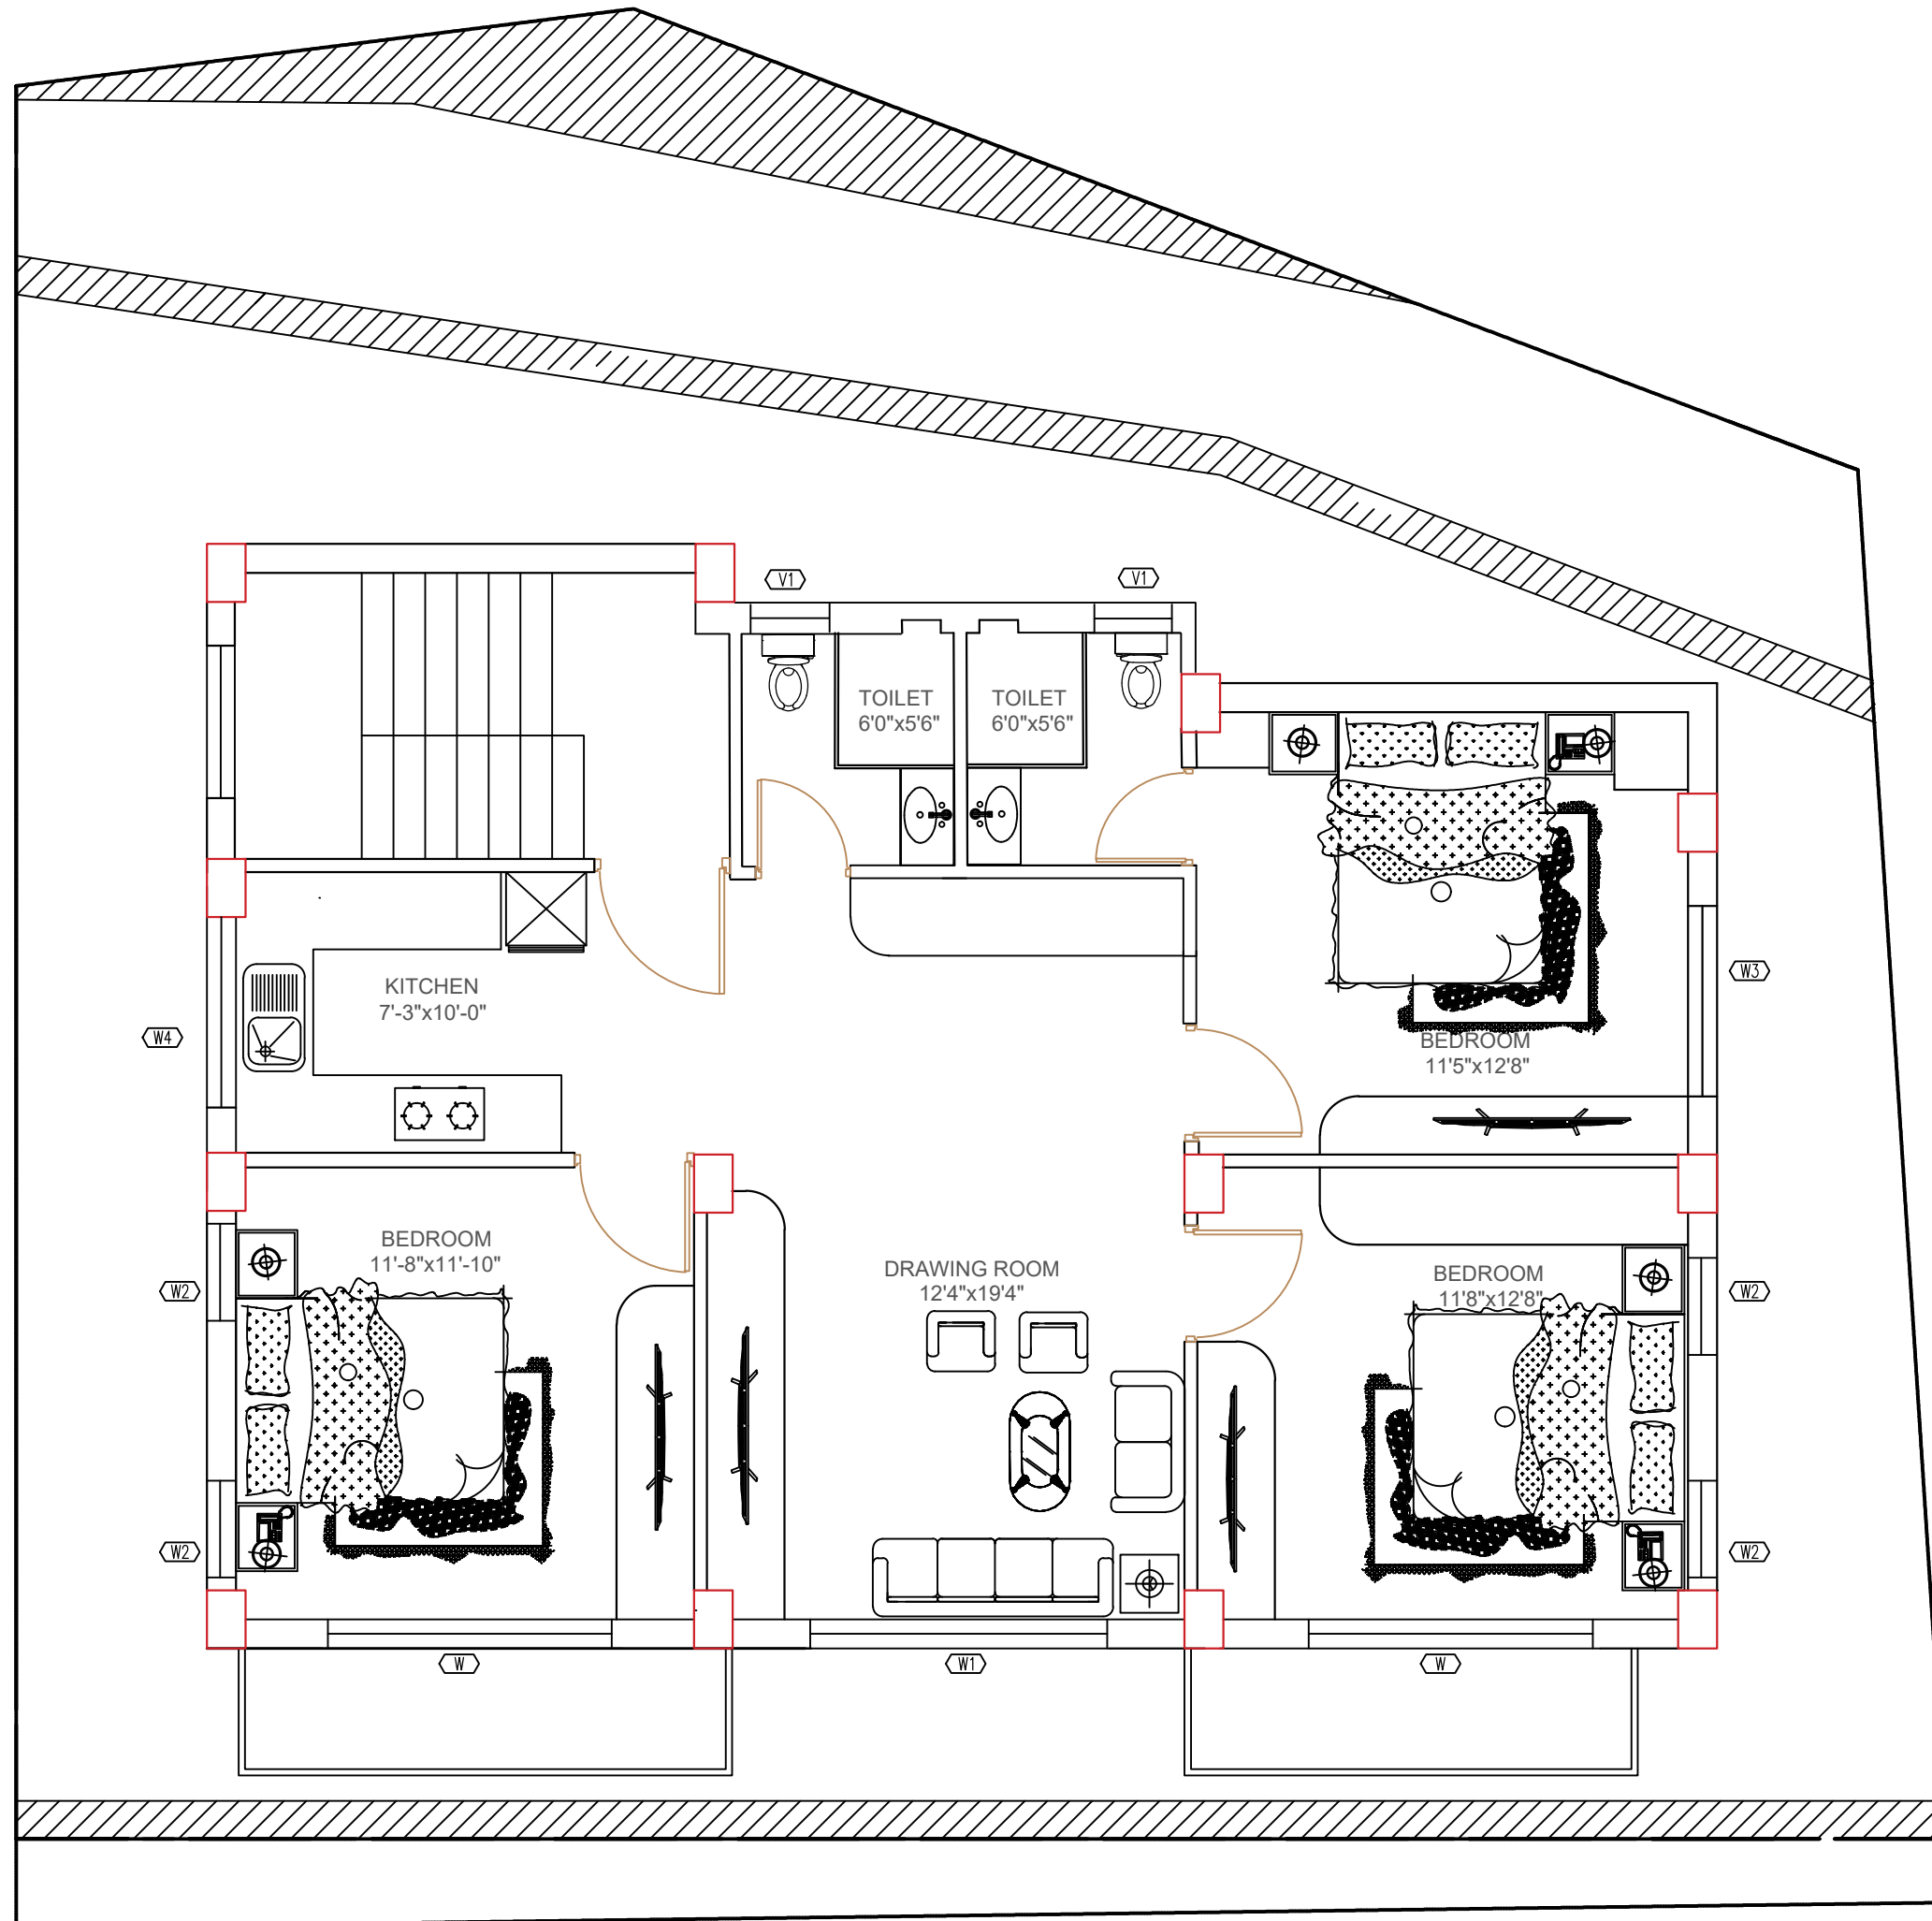

- Notes
- Dimensions are in millimeter unless stated otherwise.
 - Dimensions should be read and not measured.
 - The current version shall supersede previous drawings or revision of respective area.
 - Drawing can not be used for construction or any other purpose unless stamped as Good for construction (GFC).

- Site engineer must correlate architectural drawings and engineering drawings at site. Should a mis-match /discrepancy be found, same shall be notified immediately to the architect in writing.
- This drawing shall serve only for coordination for engineering / services discipline. Details and technical specifications must be referred from engineering/ vendor drawings for which technical ownership and responsibilities rests with relevant discipline expert.
- Intellectual copyright of the drawing shall remain with Creators Architects. No content wholly or partially should be used for any other purpose without written consent from the firm.

References
AR: Architecture
AV: Audio vedio
EL: Electrical
FR: Fire
HV: HVAC
IT: Information technology
MG: Medical gas
PL: plumbing
STR: Structure
Ven: Vendor

Issue stamp

Stage



Geolocation
PANTHAGHATI, SHIMLA

Scale 1:100
Sheet Size A1/A3

Drawing Title
WORKING DRAWING

Drawing Number Revision

1 R1
Date 27/11/2025

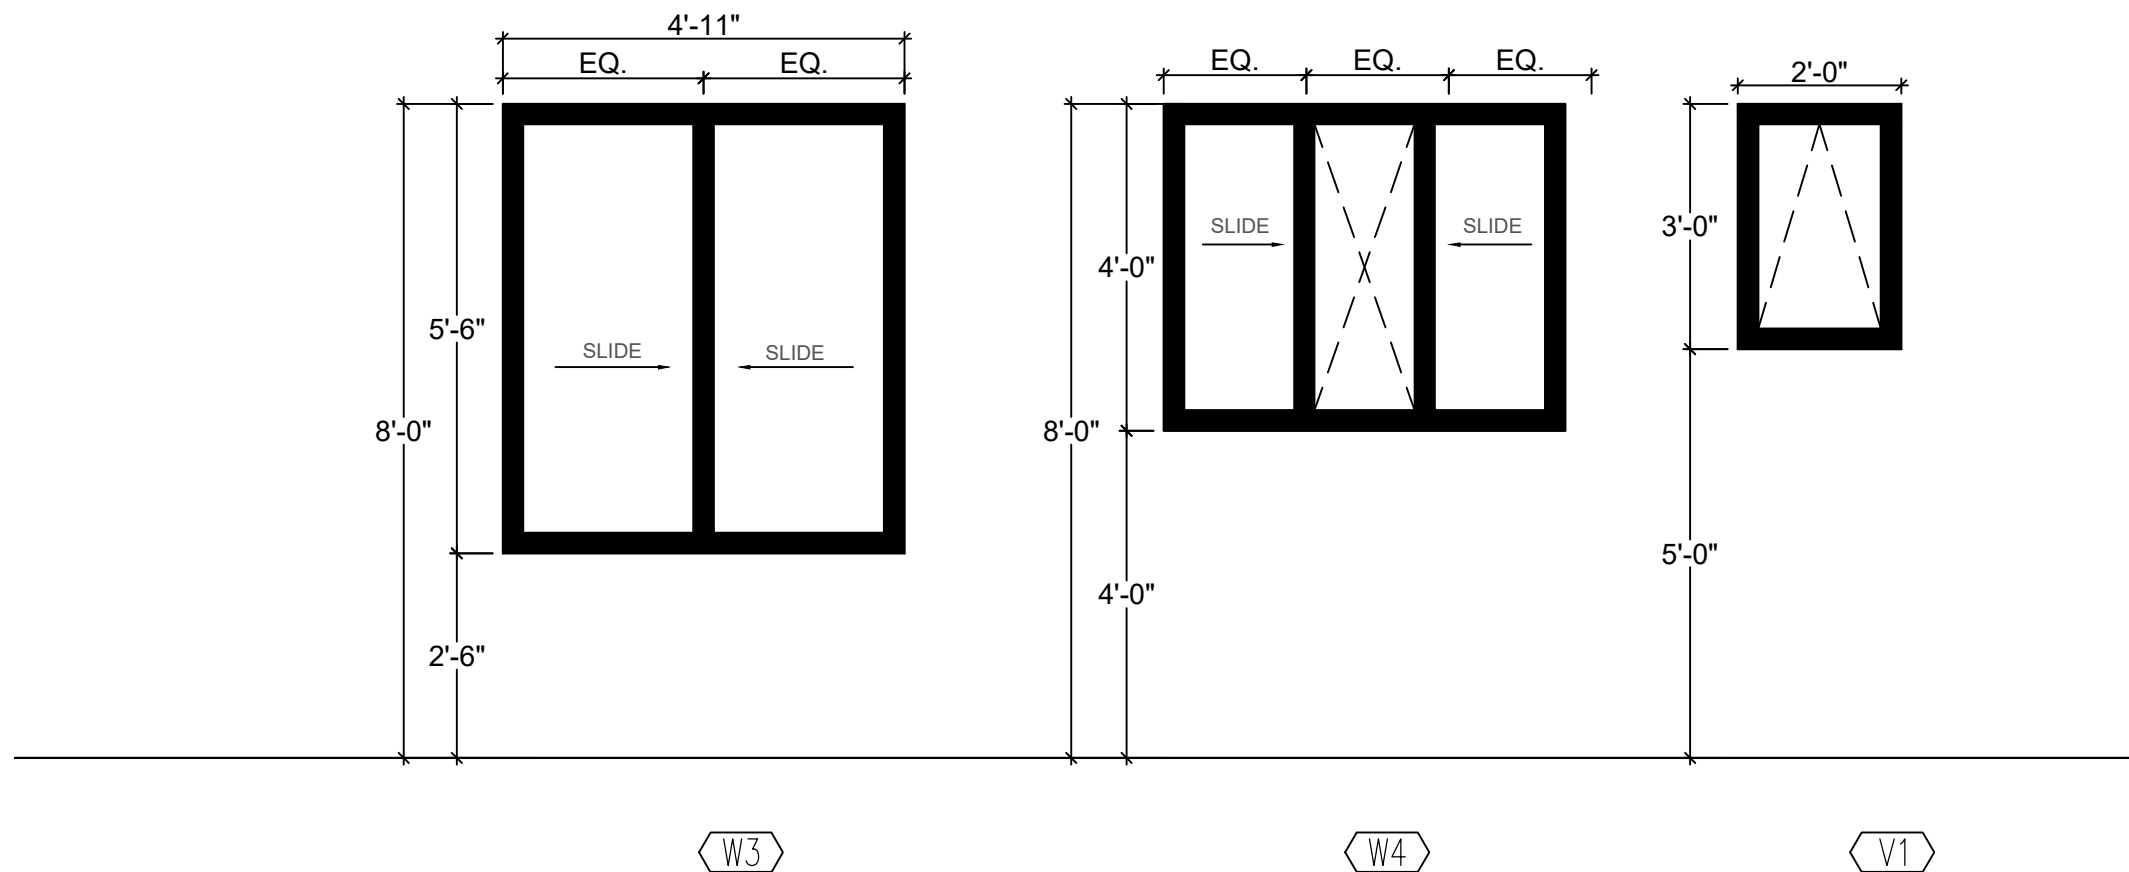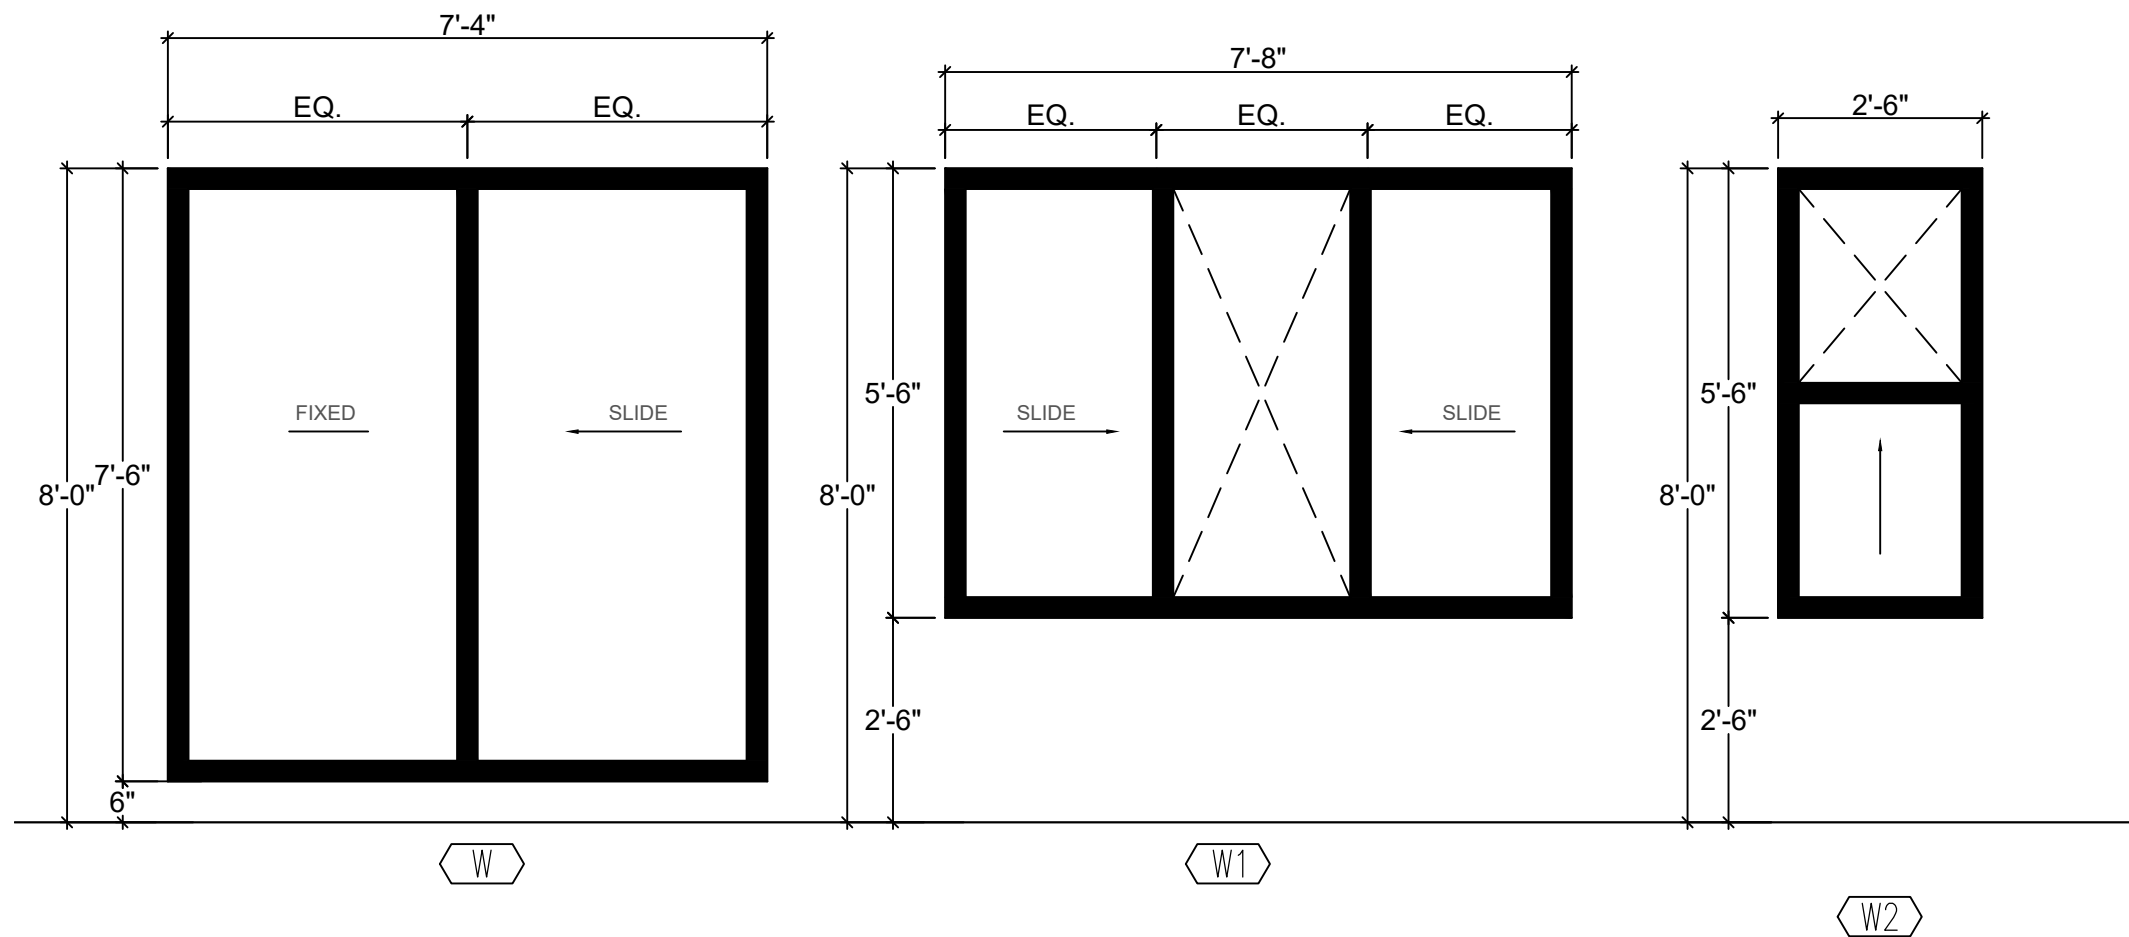

SR.NO.	DESIGNATION	NO.S	SIZE IN FEET (LENGTH X HEIGHT)	SILL LVL.	LINTEL LVL.
01	W	02	7'-4"X7'-6"	0'-6"	8'-0"
02	W1	01	7'-8"X5'-6"	2'-6"	8'-0"
03	W2	04	2'-0"X5'-6"	2'-6"	8'-0"
04	W3	01	5'-6"X5'-6"	2'-6"	8'-0"
05	W4	01	5'-2"X4'-0"	4'-0"	8'-0"
06	V1	02	2'-0"X3'-0"	5'-0"	8'-0"